


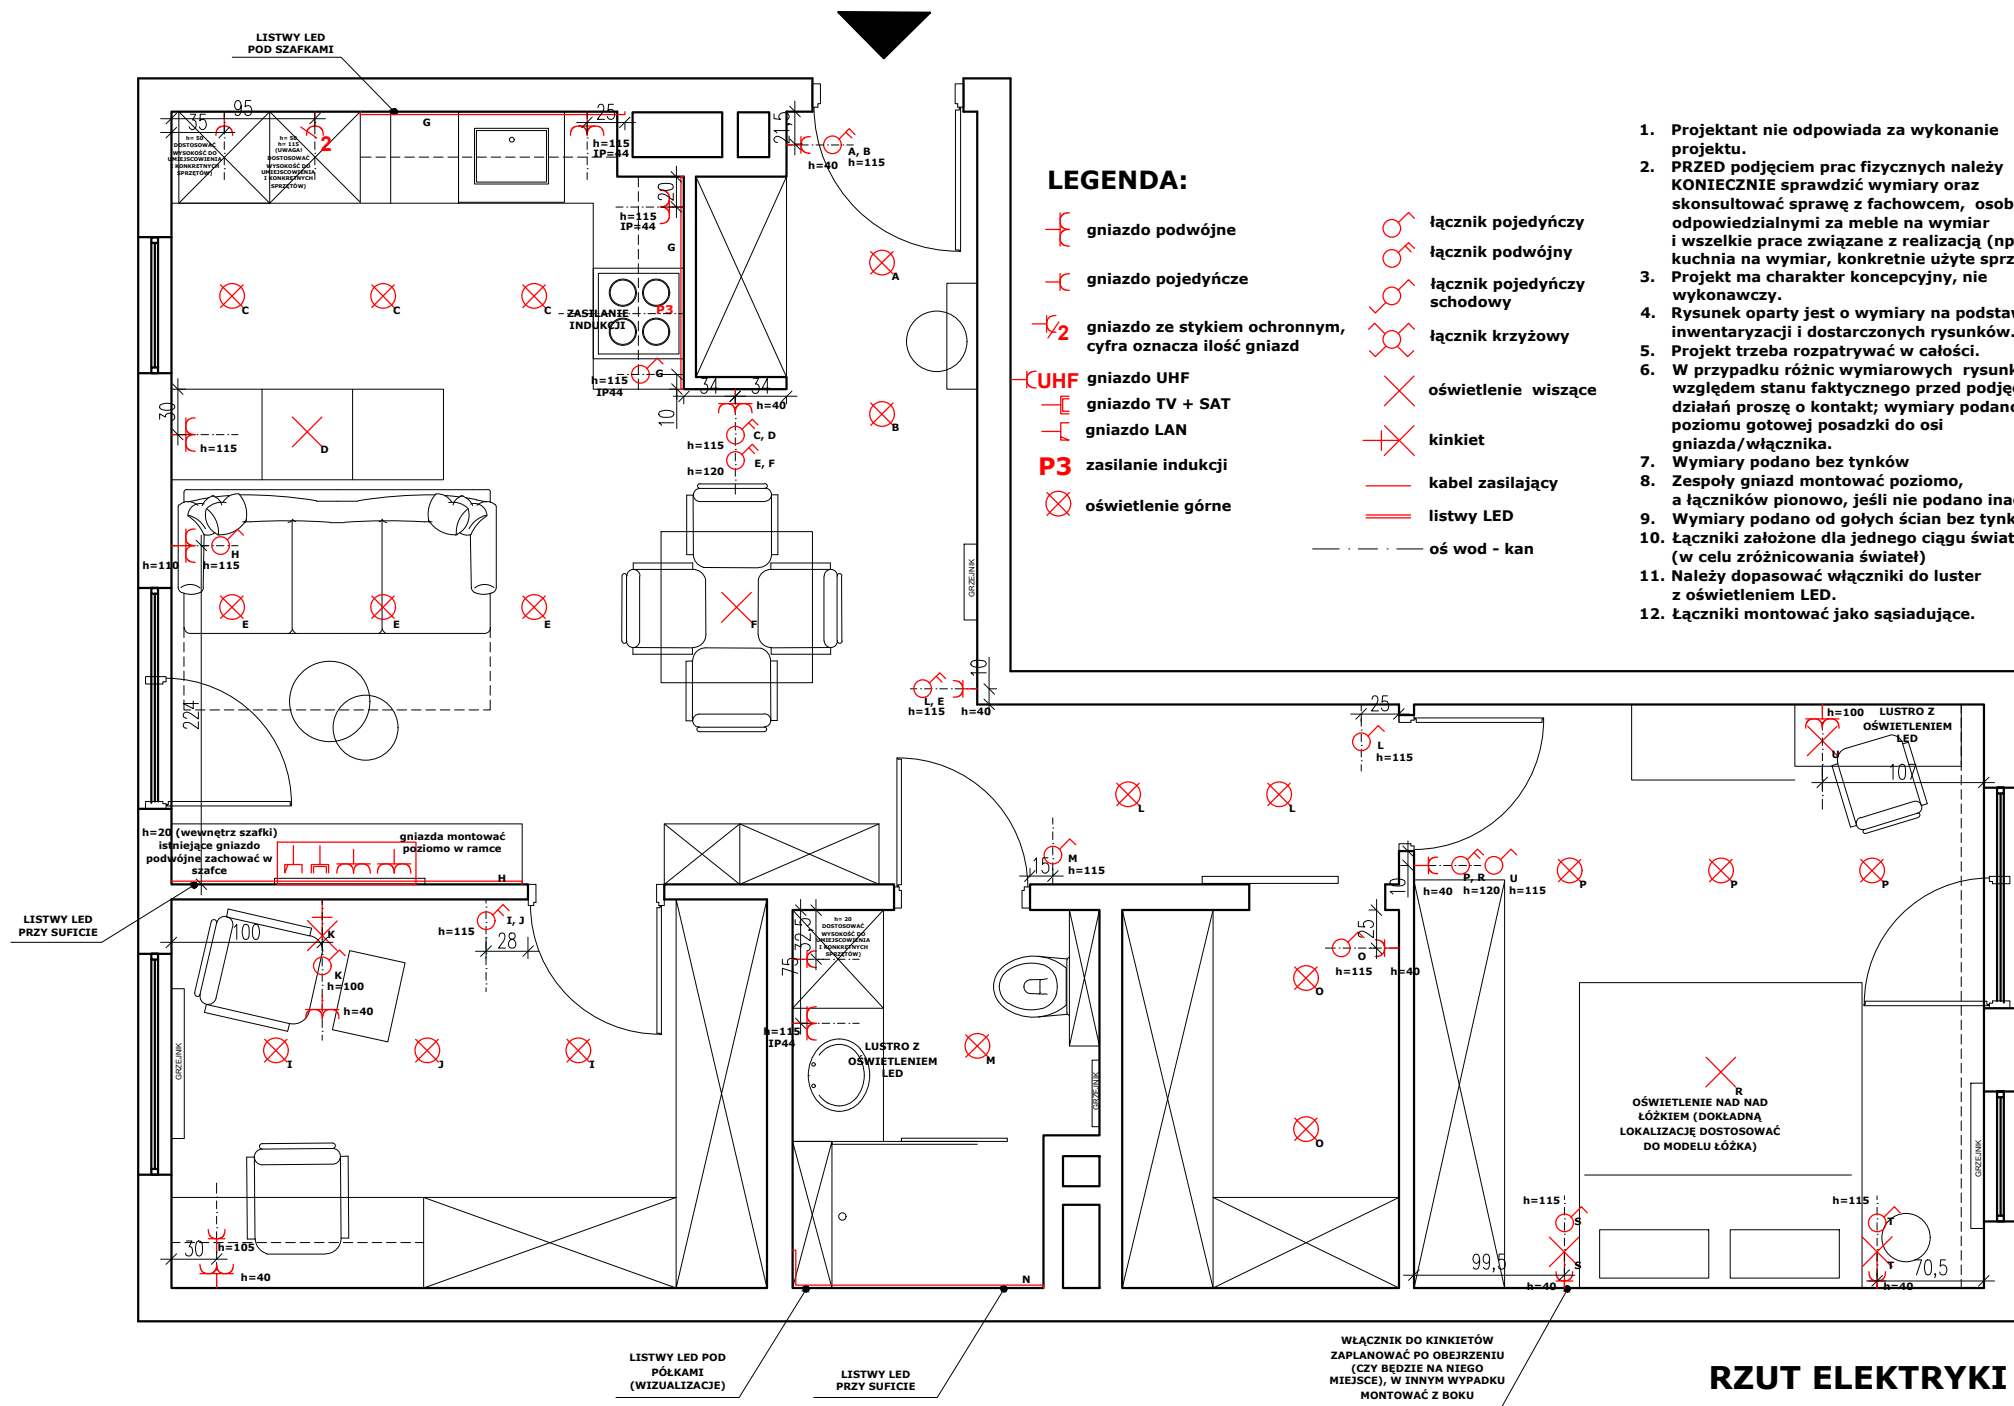

1. Projektant nie odpowiada za wykonanie projektu.
2. PRZED podjęciem prac fizycznych należy KONIECZNIE sprawdzić wymiary oraz skonsultować sprawę z fachowcem, osobami odpowiedzialnymi za meble na wymiar i wszelkie prace związane z realizacją (np. kuchnia na wymiar, konkretnie użyte sprzęty).
3. Projekt ma charakter koncepcyjny, nie wykonawczy.
4. Rysunek oparty jest o wymiary na podstawie inwentaryzacji i dostarczonych rysunków.
5. Projekt trzeba rozpatrywać w całości.
6. W przypadku różnic wymiarowych rysunku względem stanu faktycznego przed podjęciem działań proszę o kontakt; wymiary podano od poziomu gotowej posadzki do osi gniazda/włącznika.
7. Wymiary podano bez tynków
8. Zespoły gniazd montować poziomo, a łączników pionowo, jeśli nie podano inaczej.
9. Wymiary podano od gołych ścian bez tynków.
10. Łączniki założone dla jednego ciągu światła (w celu zróżnicowania światła)
11. Należy dopasować włączniki do luster z oświetleniem LED.
12. Łączniki montować jako sąsiadujące.